12–12(60, 61).

Дефекты и повреждения. Категория технического состояния

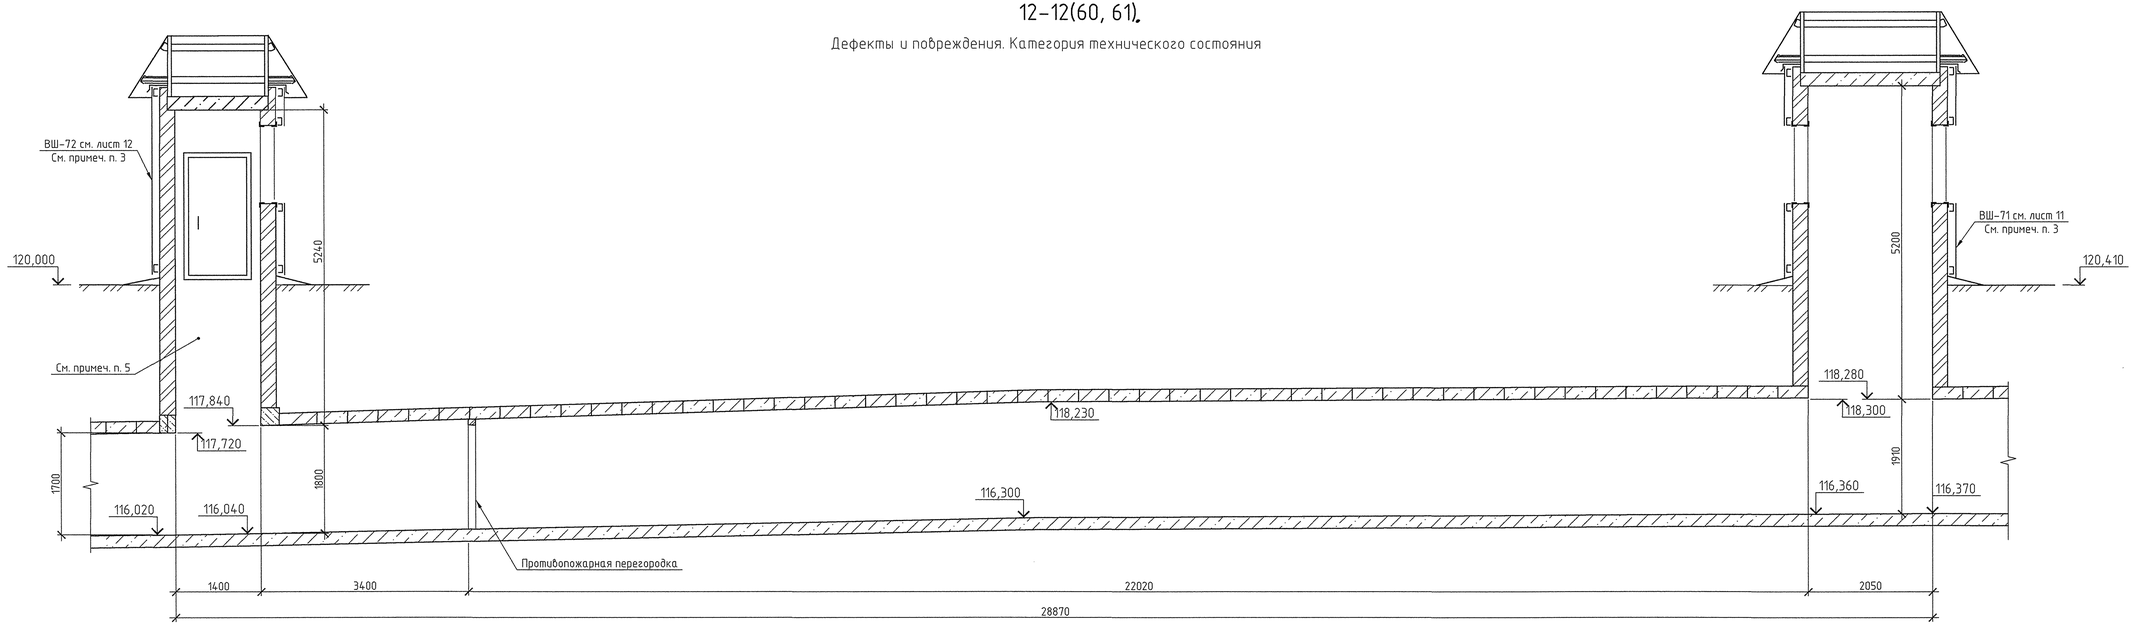

1. Условные обозначения дефектов и повреждений см. лист 57.
2. Условные обозначения категории технического состояния см. лист 17.
3. Разрушение кирпичной кладки вентиляционных шахт ВШ–71, ВШ–72 с внутренней стороны, расположенной ниже уровня земли, на отдельных участках на глубину до 120 мм, вымывание раствора швов кирпичной кладки на глубину до 60 мм.
4. Конструкцию стен, днища, перекрытия (класс арматуры, марку бетона) см. Заключение.
5. Стальная площадка и стремянка для спуска в тоннель условно не показаны.

						289845-ОСК	
						ОАО "Новолипецкий металлургический комбинат"	
Изм.	Кол.уч.	Лист	№ док.	Подп.	Дата		
Разраб.		Тимирязева			05.16	ТЭЦ. Установка турбогенератора № 5. Техническое перевооружение. Участки электрокабельных тоннелей: КТ–33, КТ–34, КТ–45, КТ–44, КТ–38, КТ–39, КТ–40, КТ–41	Стадия: — / Лист: 63 / Листов: —
Проверил		Кукин			05.16		
Гл. спец		Собко			05.16		
Н. контр.		Пурко			05.16	Разрез 12–12. Дефекты и повреждения. Категория технического состояния	Гипромез Липецкий, Группа НЛМК
ГИП		Бубнов			05.16		

Формат А4х4

Согласовано

Взам. инв. №

Подп. и дата

Инв. № подл.